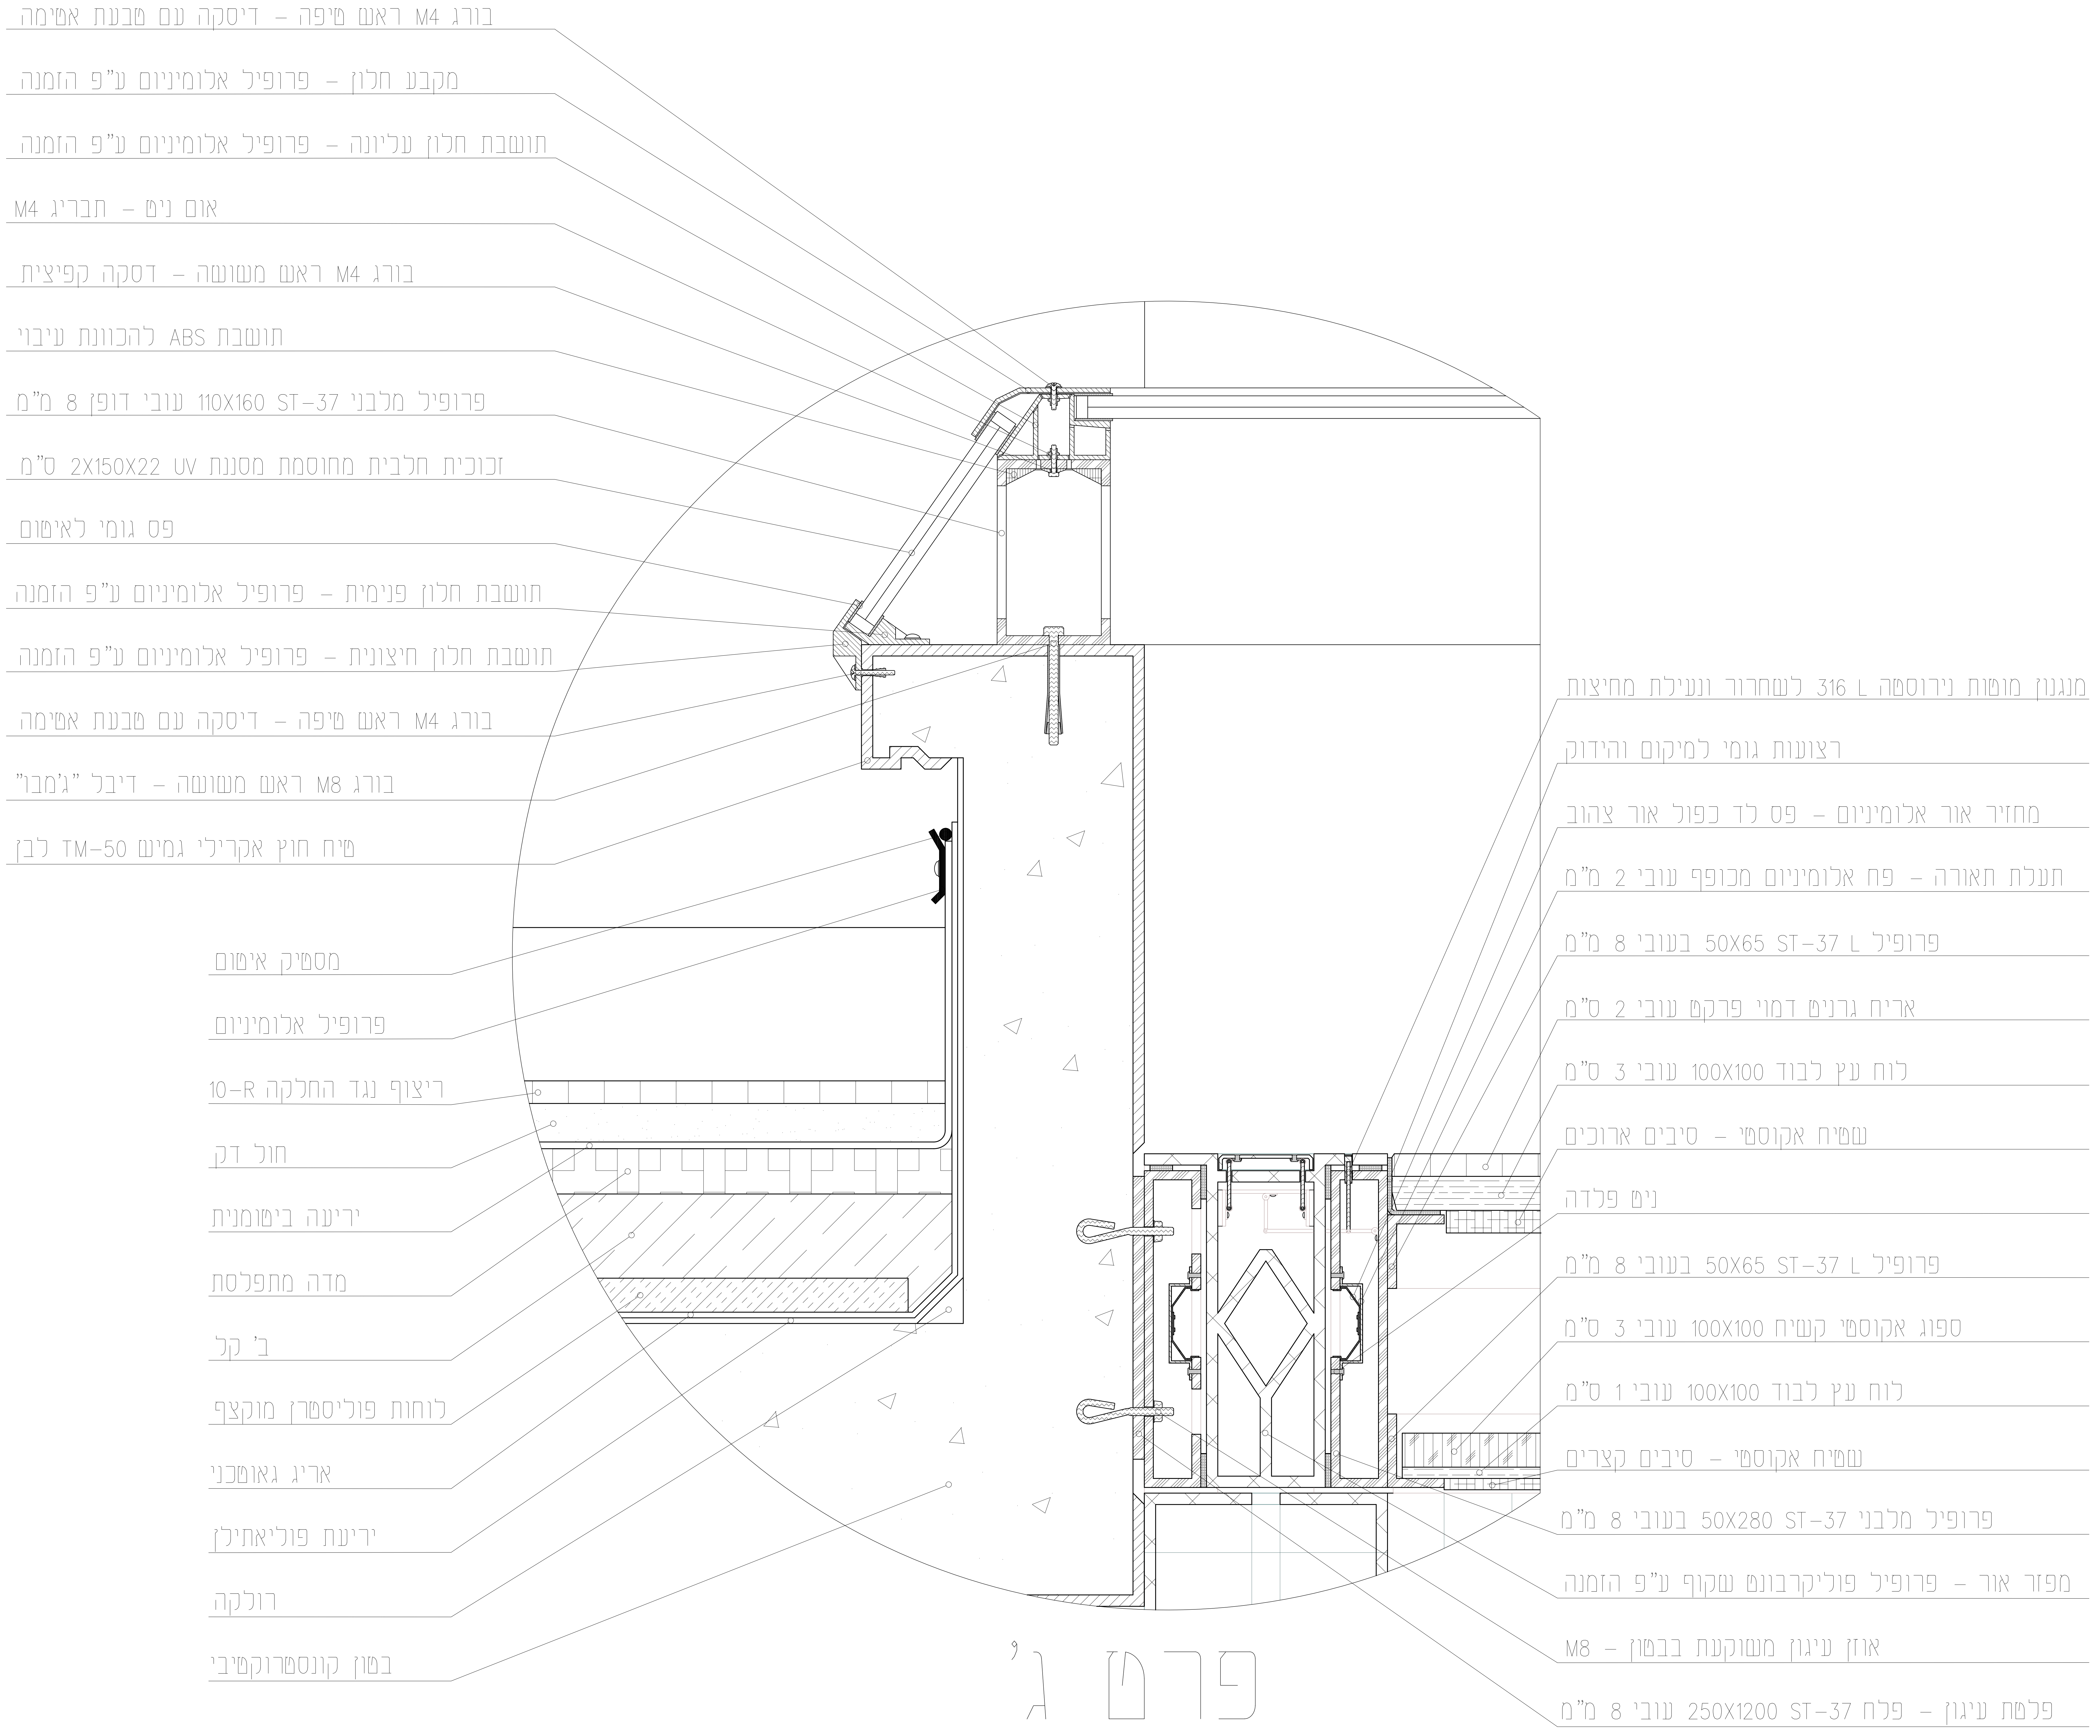
בורג M4 ראש טיפה - דיסקה עם טבעת אטימה
מקבע חלון - פרופיל אלומיניום ע"פ הזמנה
תושבת חלון עליונה - פרופיל אלומיניום ע"פ הזמנה
אום ניט - תבריג M4
בורג M4 ראש משושה - דסקה קפיצית
תושבת ABS להכוונת עיבוי
פרופיל מלבני ST-37 110X160 עובי דופן 8 מ"מ
זכוכית חלבית מחוסמת מסננת UV 2X150X22 ס"מ
פס גומי לאיטום
תושבת חלון פנימית - פרופיל אלומיניום ע"פ הזמנה
תושבת חלון חיצונית - פרופיל אלומיניום ע"פ הזמנה
בורג M4 ראש טיפה - דיסקה עם טבעת אטימה
בורג M8 ראש משושה - דיבל "ג'מבו"
טיח חוץ אקרילי גמיש TM-50 לבן
מסטיק איטום
פרופיל אלומיניום
ריצוף נגד החלקה R-10
חול דק
יריעה ביטומנית
מדה מתפלסת
ב' קל
לוחות פוליסטרן מוקצף
אריג גאוטכני
יריעת פוליאתילן
רולקה
בטון קונסטרוקטיבי
מנגנון מוטות נירוסטה L 316 לשחרור ונעילת מחיצות
רצועות גומי למיקום והידוק
מחזיר אור אלומיניום - פס לד כפול אור צהוב
תעלת תאורה - פח אלומיניום מכופף עובי 2 מ"מ
פרופיל L ST-37 50X65 בעובי 8 מ"מ
אריח גרניט דמוי פרקט עובי 2 ס"מ
לוח עץ לבוד 100X100 עובי 3 ס"מ
שטיח אקוסטי - סיבים ארוכים
ניט פלדה
פרופיל L ST-37 50X65 בעובי 8 מ"מ
ספוג אקוסטי קשיח 100X100 עובי 3 ס"מ
לוח עץ לבוד 100X100 עובי 1 ס"מ
שטיח אקוסטי - סיבים קצרים
פרופיל מלבני ST-37 50X280 בעובי 8 מ"מ
מפזר אור - פרופיל פוליקרבונט שקוף ע"פ הזמנה
אוזן עיגון משוקעת בבטון - M8
פלטת עיגון - פלח ST-37 250X1200 עובי 8 מ"מ

פרט ג'

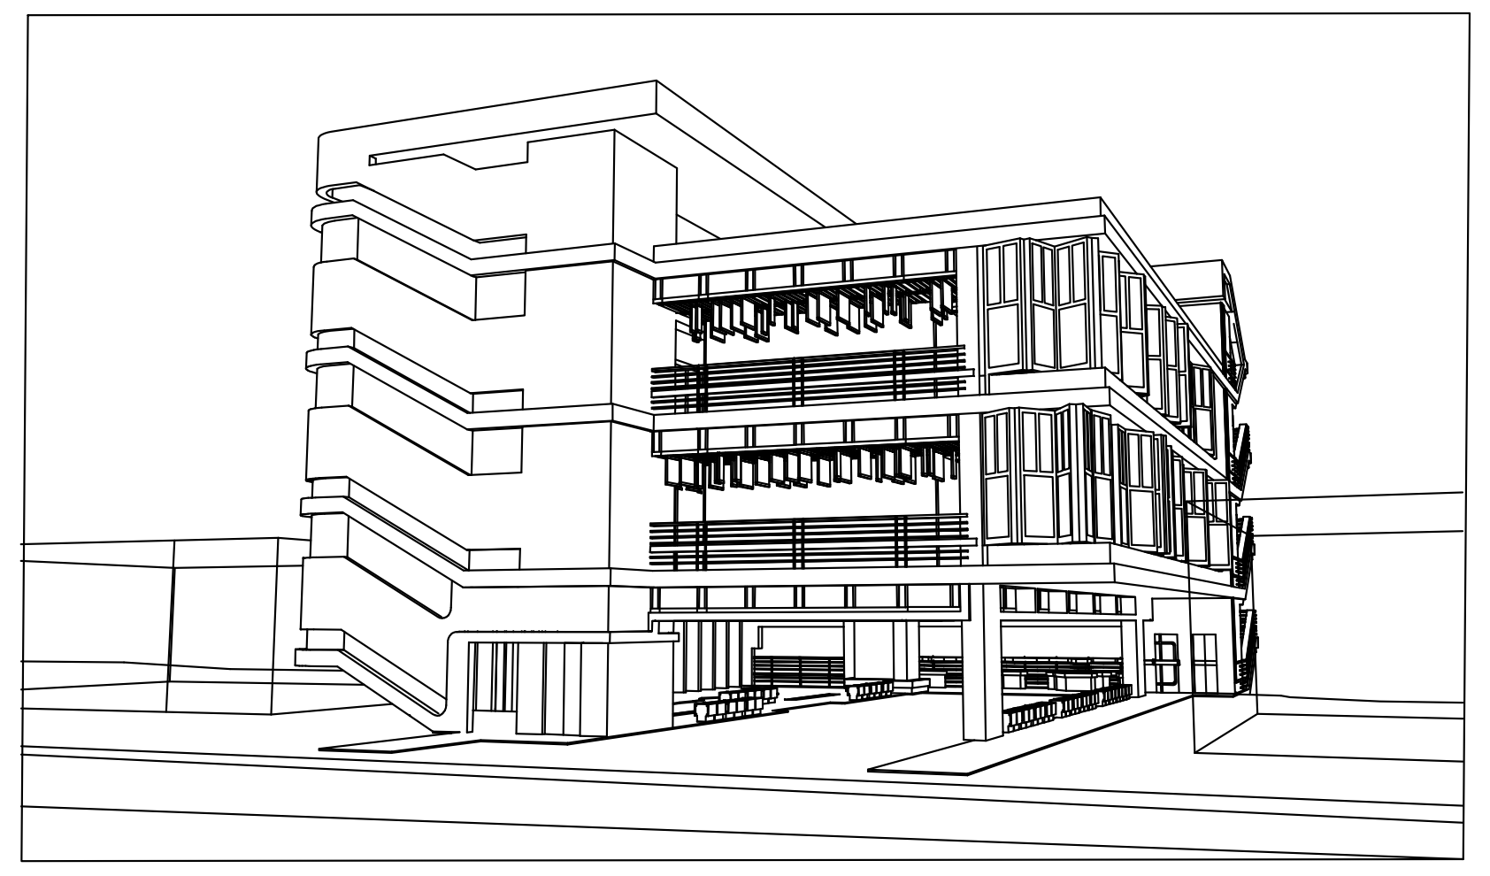

מרפאה
אוניברסיטאית

סטודיו טכנולוגי 5

מקרא

קרקע	▨	פלדה ST 37	▨
אריחים	▥	נירוסטה 316	▨
חול דק	░	ABS	▥
מדה מתפלסת	▦	גומי לאיטום	▤
ב' קל	▨	פלדה רכה	░
פוליסטירן מוקצף	▨	פוליקרבונט שקוף	▩
טיח חוץ	▨	עץ לבוד	▤
בטון קונסטרוקטיבי	░	שטיח אקוסטי	▦
		ספוג אקוסטי	▥

רשימת תפוצה

בעל תפקיד / תאריך	מנהל פרויקט	לקוח	אדריכלות	קונסטרוקציה	חשמל	מכונות	אינסטלציה	פיתוח ונ"ע	תנועה	בטיחות	נוף	אחר	

עדכונים ושינויים (מהדורות)

מהדורה	1	2	3	4	5	6	7
תאריך							

המבצע אחראי לבדיקת התכניות ולהתאמתן במקום.
על המבצע לבקר את כל המידות ולהודיע למשרד המתכנן על כל טעות או אי-התאמה. אין לקבוע מידה ע"י מדידה בשרטוט.
מהנדס/יועץ המשתמש בתכנית זו כרקע לתכניתו ואשר שמו רשום בנוסף לשם האדריכל- נושא לבדו באחריות המקצועית והחוקית לתכנית.
אסור בהחלט להשתמש בתכנית או ברעיונות הגלומים בה ללא אישור מראש בכתב מאת המתכנן.

חתך א'-א' - פרט ג

גליון 9	קנ"מ 1:5

● לעיון ○ לאישור ○ למכרז ○ לביצוע

מהדורה - 5 ב	14/9/17

מנחים | אדר' לואיס סוקולובסקי
אדר' רולה בשארה בראנסי | אדר' אורלי כהן מואס
אדר' אורית אופק-פיינדמן | אדר' מיכה רונה

דורון אנהנג | 200679330
שנה ג' | סמסטר ב

אוניברסיטת
אריאל