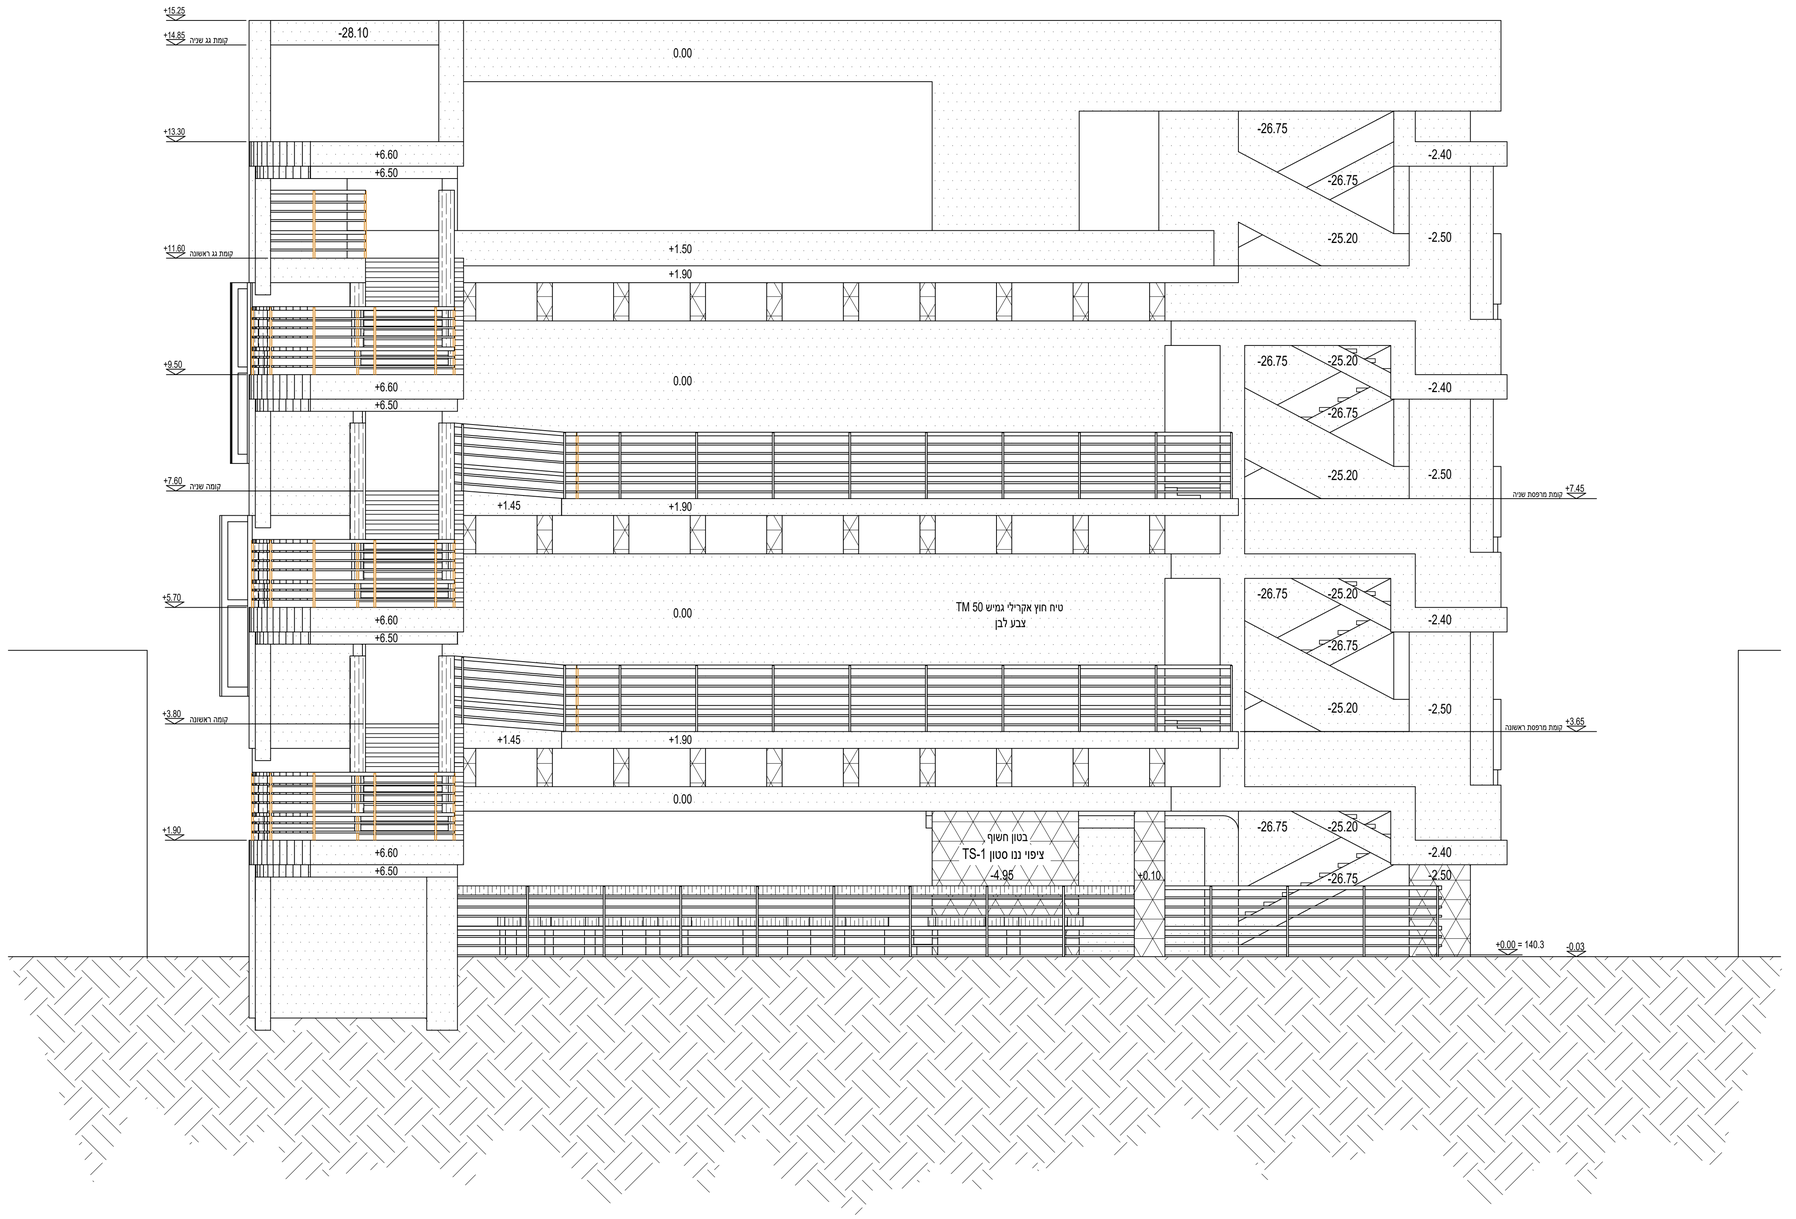

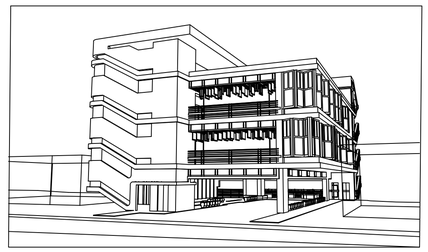

מרפאה
אוניברסיטאית

סטודיו טכנולוגי 5

מקרא

- קרקע
- טיח חוץ
- בטון חשוף
- עץ טיק

עומקים בחזית +0.10

גבהים בחזית +3.80

הפניה לרשימות

רשימת תפוצה

תאריך	בעל תפקיד	מהנדס קונסטרוקציה	אדריכלית	יזמית	חשמל	אינסטלציה	פיתוח וע"ג	תוכנה	בניהול	נוף	אחר

רשימת תפוצה (נמענים) | נושא | תאריך

המבנע אחראי לבדיקת התכנית והתאמתן במקום.
על המבנע לבקר את כל הפרטים ולהודיע למשרד המתכנן על כל טעות או אי-התאמה. אין לקבוע מידה ע"י מדידה בשרטוט.
מהנדס/יועץ המשתמש בתכנית זו ברקע למכרזים ואשר שמו רשום בנוסף לשם האדריכל – נושא לכדי באחריות המקצועית והחוקית לתכנית.
אסור בהחלט להשתמש בתכנית או בריענות הנלמדים בה ללא אישור מראש ובכתב מאת המתכנן.

חזית צפונית

גליון 4	קנ"מ 1:50

לעיון ● | לאישור ○ | למכרז ○ | לביצוע ○

מהדורה - 5 ב	14/9/17

מנחים | אדר' לואיס סוקולובסקי
אדר' רולה בשארה בראנסי | אדר' אורלי כהן מואס
אדר' אורית אופק-פיינדמן | אדר' מיכה רונה

דורון אנהנג | 200679330
שנה ג' | סמסטר ב

N

אוניברסיטת
אריאל