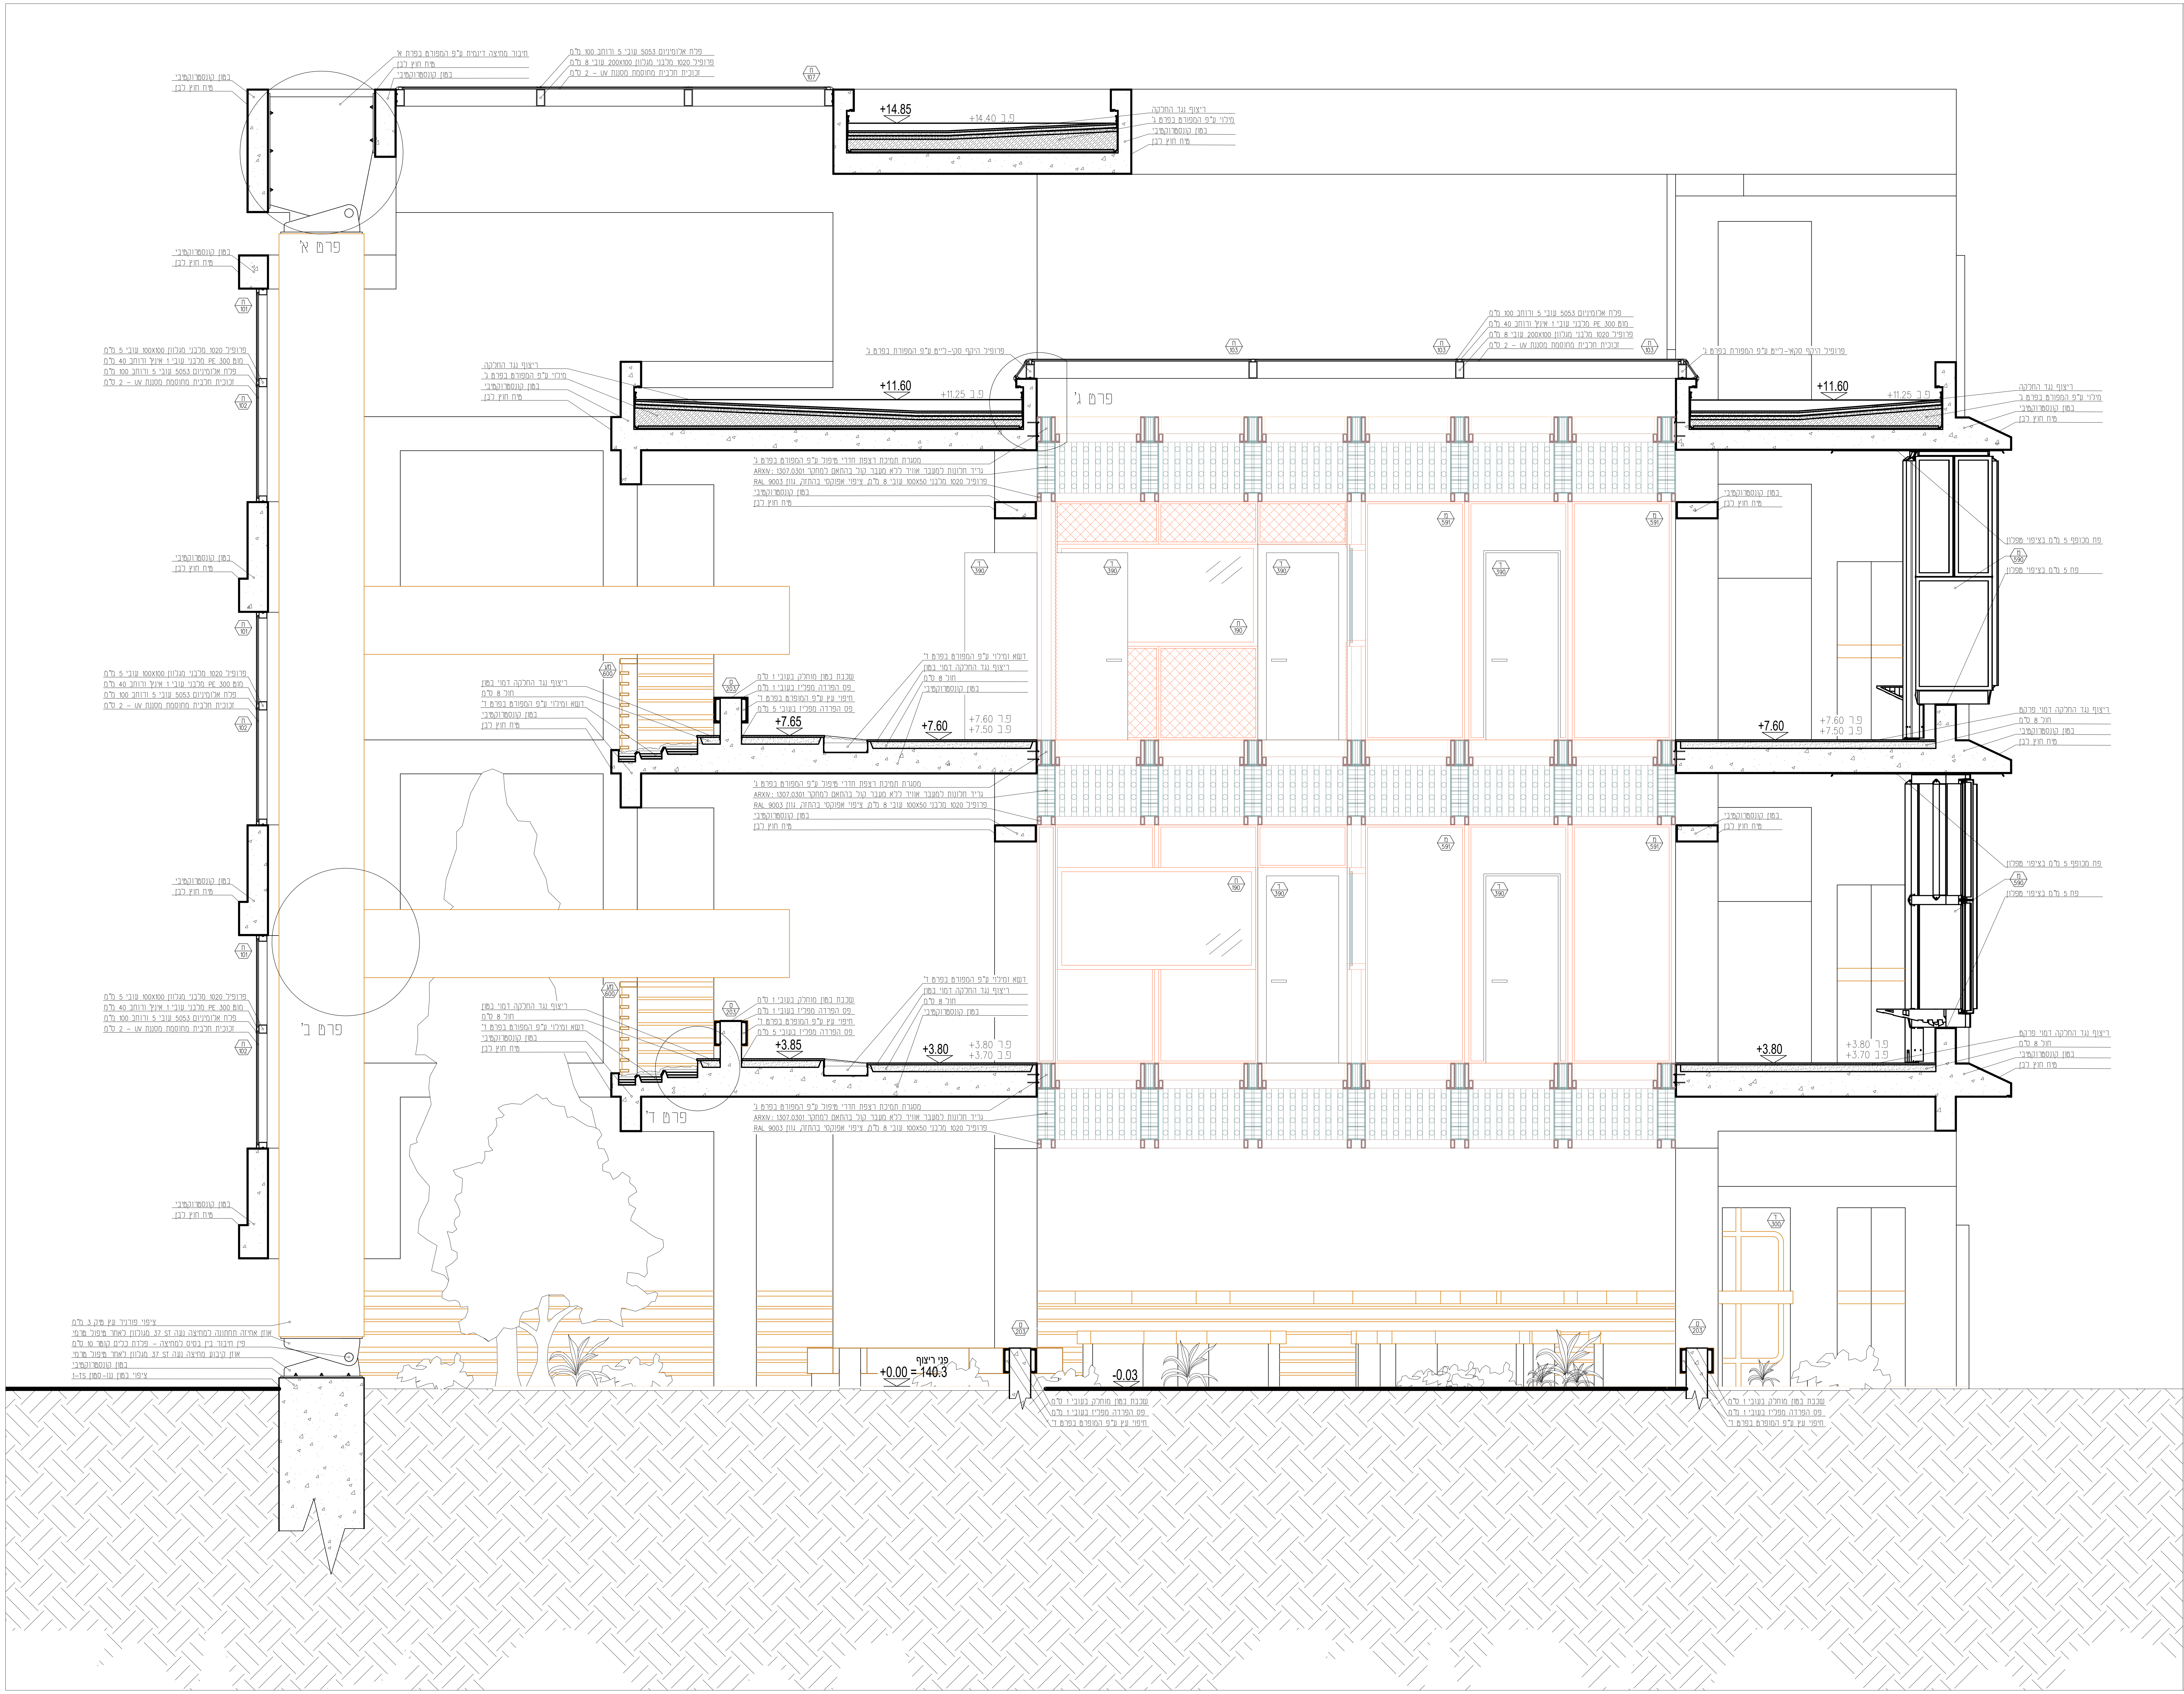

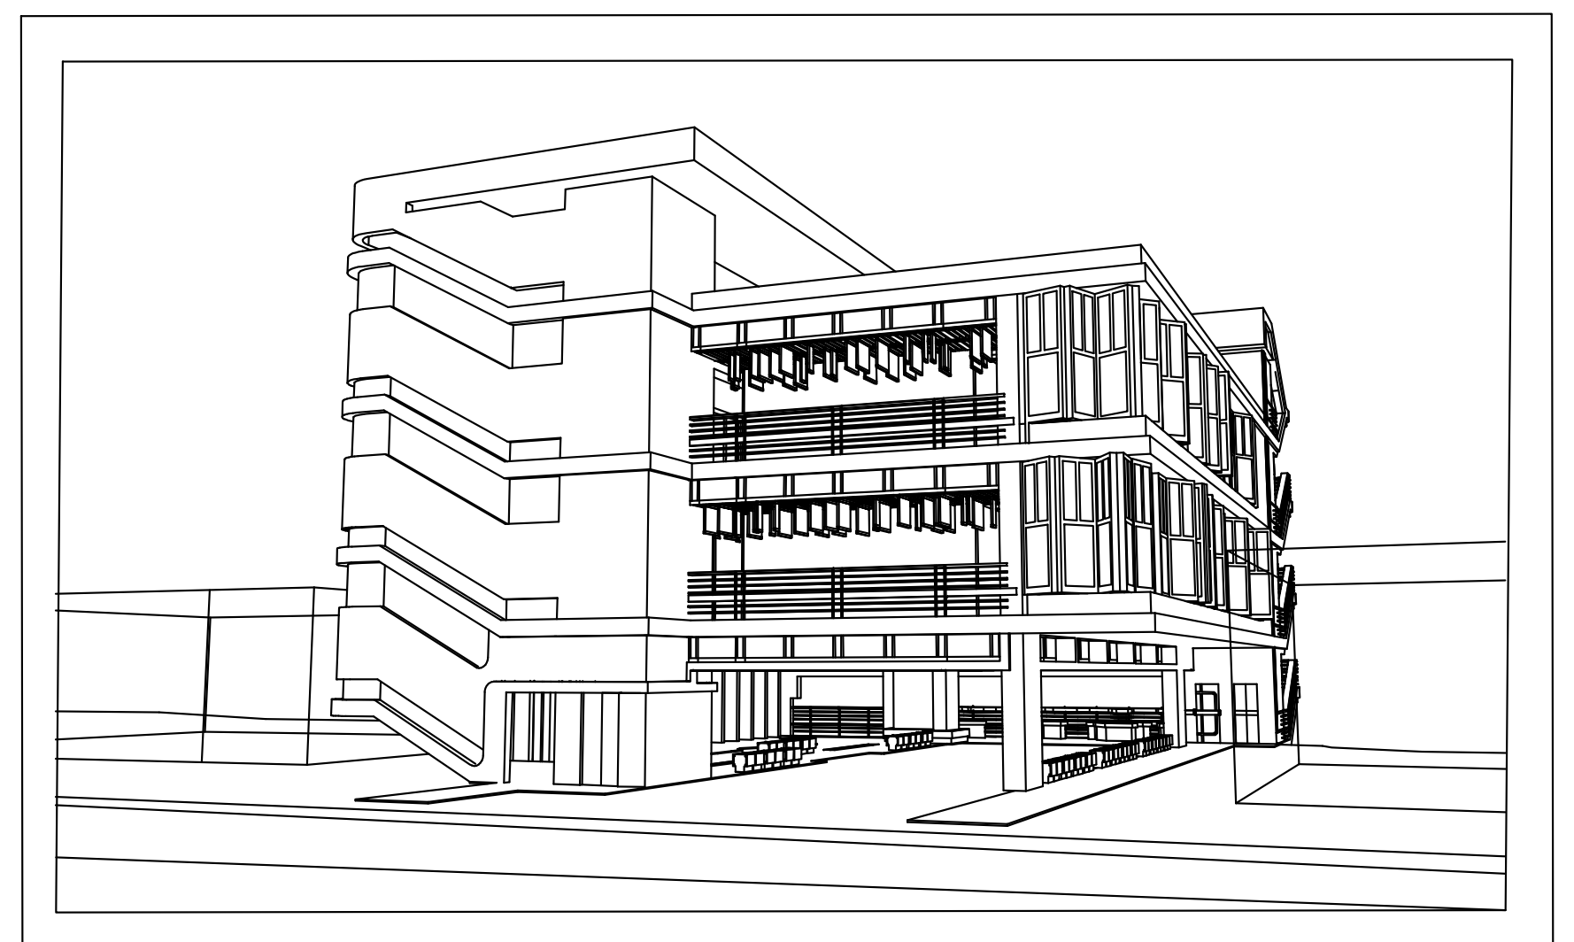

מרפאה
אוניברסיטאית

סטודיו טכנולוגי 5

מקרא

קרקע	▨
אריחים	▥
חול דק	▒
מדה מתפלסת	▦
ב' קל	▨
פוליסטירן מוקצף	▨
טיח חוץ	▨
בטון קונסטרוקטיבי	▒

סימון הפניה לפרט

+3.80 גבהים בחתך

הפניה לרשימות

רשימת תפוצה

בעל תפקיד / תאריך	מנהל פרויקט	לקוח	אדריכלות	קונסטרוקציה	חשמל	מכונות	אינסטלציה	פיתוח וע"ע	תנועה	בטיחות	נוף	אחר	

עדכונים ושינויים (מהדורות)

מהדורה	1	2	3	4	5	6	7
תאריך							

המבצע אחראי לבדיקת התכניות ולהתאמתן במקום.
על המבצע לבקר את כל המידות ולהודיע למשרד המתכנן על כל טעות או אי-התאמה. אין לקבוע מידה ע"י מדידה בשרטוט.
מהנדס/יועץ המשתמש בתכנית זו כרקע לתכניתו ואשר שמו רשום בנוסף לשם האדריכל- נושא לבדו באחריות המקצועית והחוקית לתכנית.
אסור בהחלט להשתמש בתכנית או ברעיונות הגלומים בה ללא אישור מראש בכתב מאת המתכנן.

חתך א'-א' - מפורט

גליון 8 | קנ"מ 1:25

לעיון ● | לאישור ○ | למכרז ○ | לביצוע ○

מהדורה - 5 ב | 14/9/17

מנחים | אדר' לואיס סוקולובסקי
אדר' רולה בשארה בראנסי | אדר' אורלי כהן מואס
אדר' אורית אופק-פיינדמן | אדר' מיכה רונה

דורון אנהנג | 200679330
שנה ג' | סמסטר ב

אוניברסיטת
אריאל