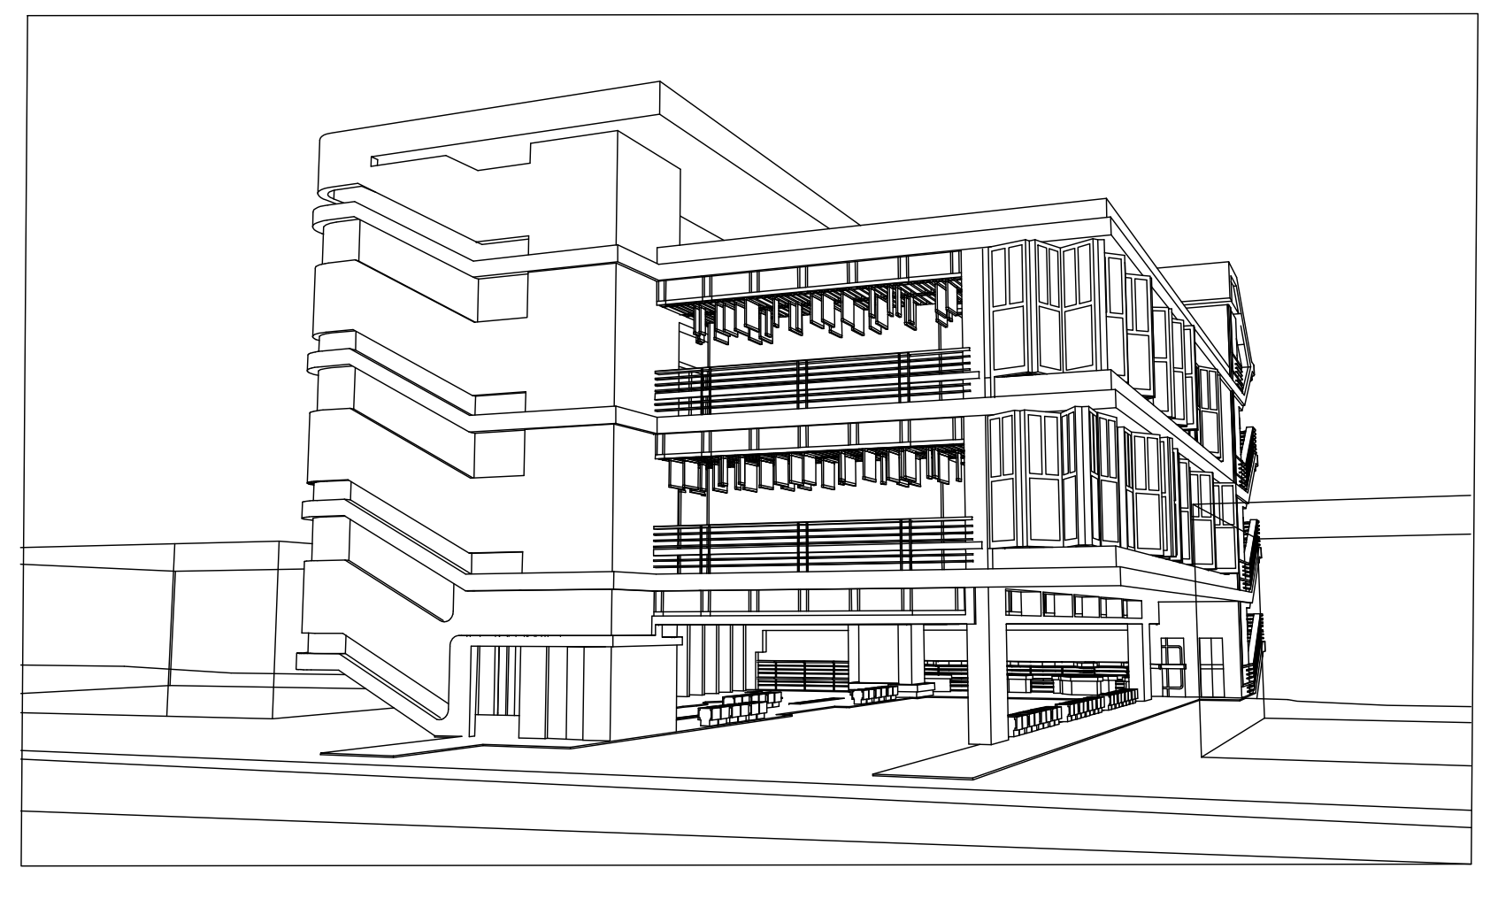

מרפאה אוניברסיטאית

סטודיו טכנולוגי 5

מקרא

סימון הפניה לפרטי

▤	עץ טיק
▥	אריחים
☐	חול דק
⠿	בטה מתפלסת
▨	פלדה ST 37
▭	עץ לבוד
▨	טיח חוץ
⠿	בטון קונסטרוקטיבי
+3.80	גבהים בחתך
203	הפניה לרשימות

עדכונים ושינויים (מהדורות)

מהדורה	תאריך	
1		
2		
3		
4		
5		
6		
7		

רשימת תפוצה

בעל תפקיד / תאריך	מנהל פרויקט	לקוח	אדריכלות	קונסטרוקציה	חשמל	מכונות	אינסטלציה	פיתוח וע"ע	תנועה	בטיחות	נוף	אחר	

המבצע אחראי לבדיקת התכניות ולהתאמתן במקום.
על המבצע לבקר את כל המידות ולהודיע למשרד המתכנן על כל טעות או אי–התאמה. אין לקבוע מידה ע"י מדידה בשרטוט.
מהנדס/יועץ המשתמש בתכנית זו כרקע לתכניתו ואשר שמו רשום בנוסף לשם האדריכל– נושא לבדו באחריות המקצועית והחוקית לתכנית.
אסור בהחלט להשתמש בתכנית או ברעיונות הגלומים בה ללא אישור מראש בכתב מאת המתכנן.

חתך ב'-ב' - גיליון מדרגות

גליון 11	ע"פ המצוין בשרטוט
● לעיון ○ לאישור	○ למכרז ○ לביצוע
מהדורה - 5 ב	14/9/17

מנחים | אדר' לואיס סוקולובסקי
אדר' רולה בשארה בראנסי | אדר' אורלי כהן מואס
אדר' אורית אופק-פיינדמן | אדר' מיכה רונה

דורון אנהנג | 200679330
שנה ג' | סמסטר ב

אוניברסיטת אריאל

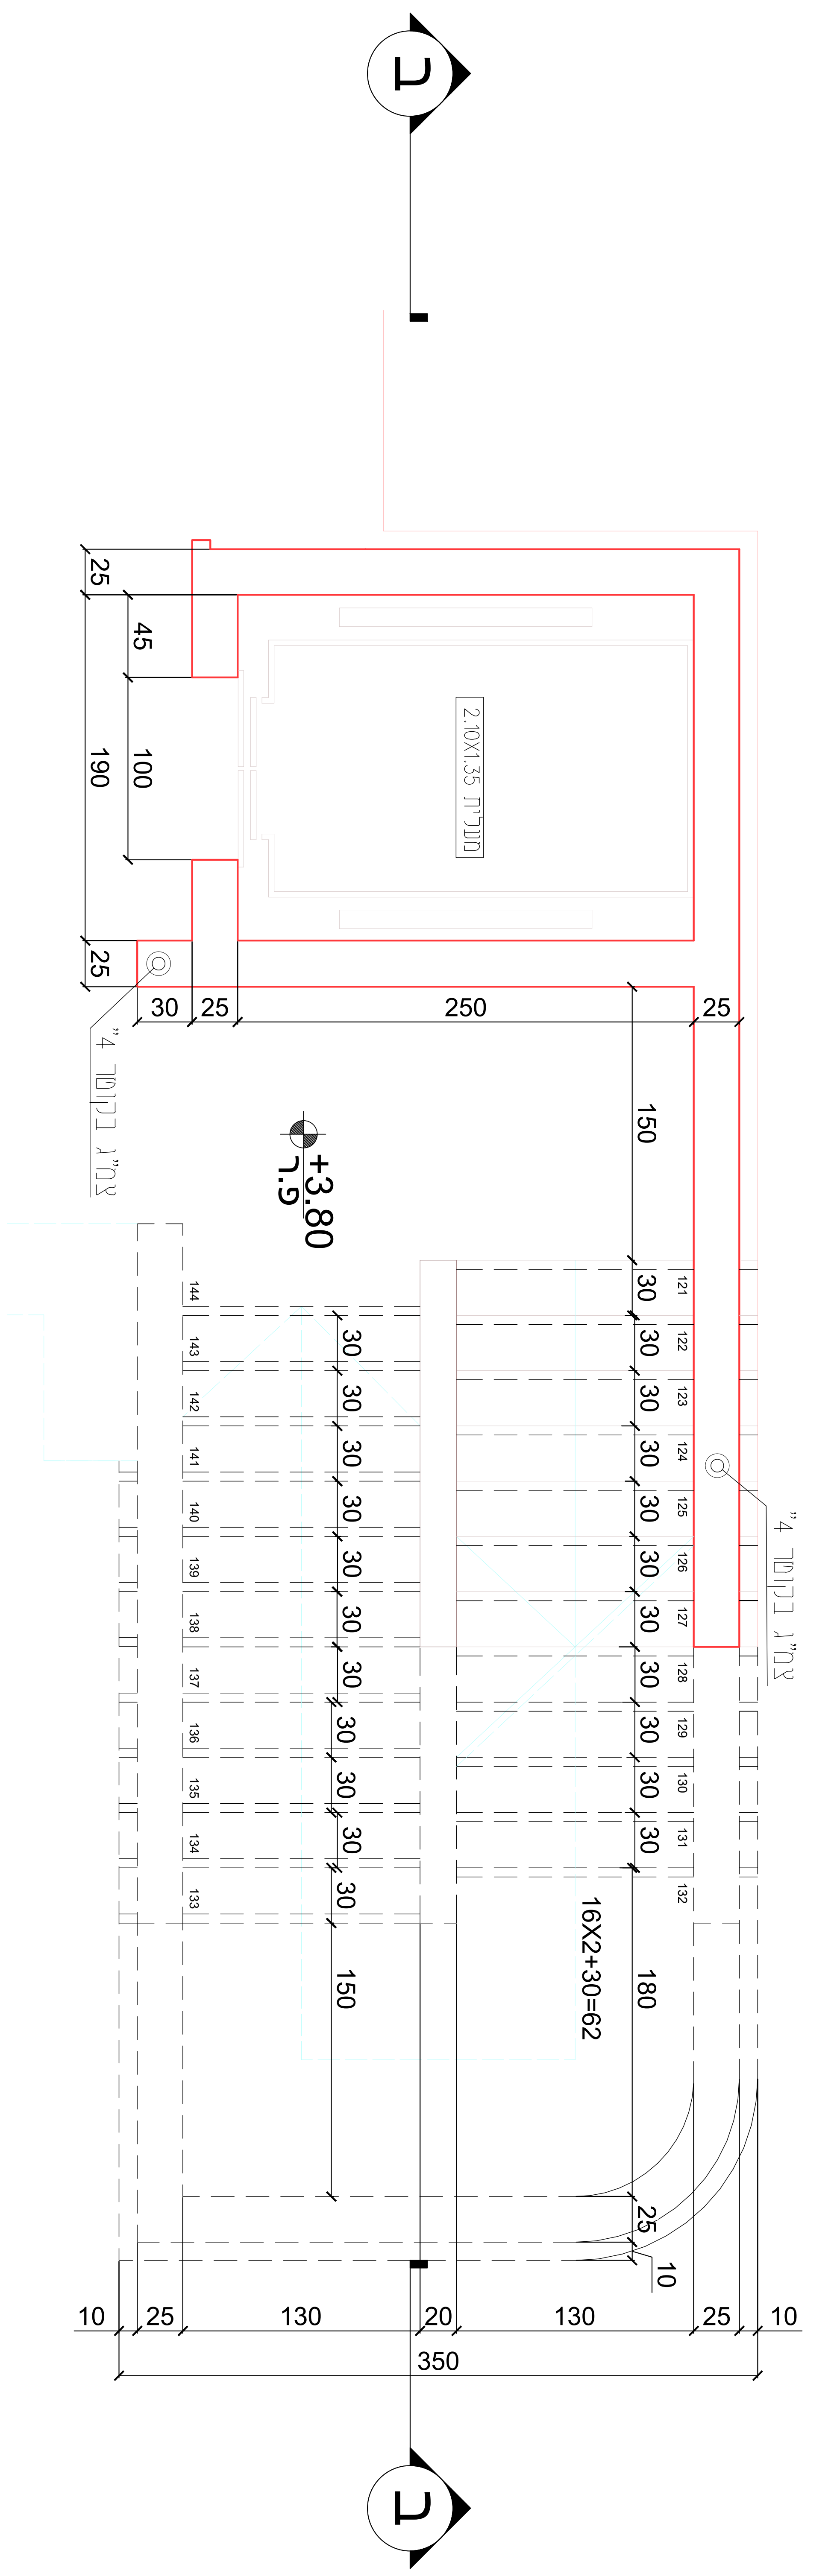

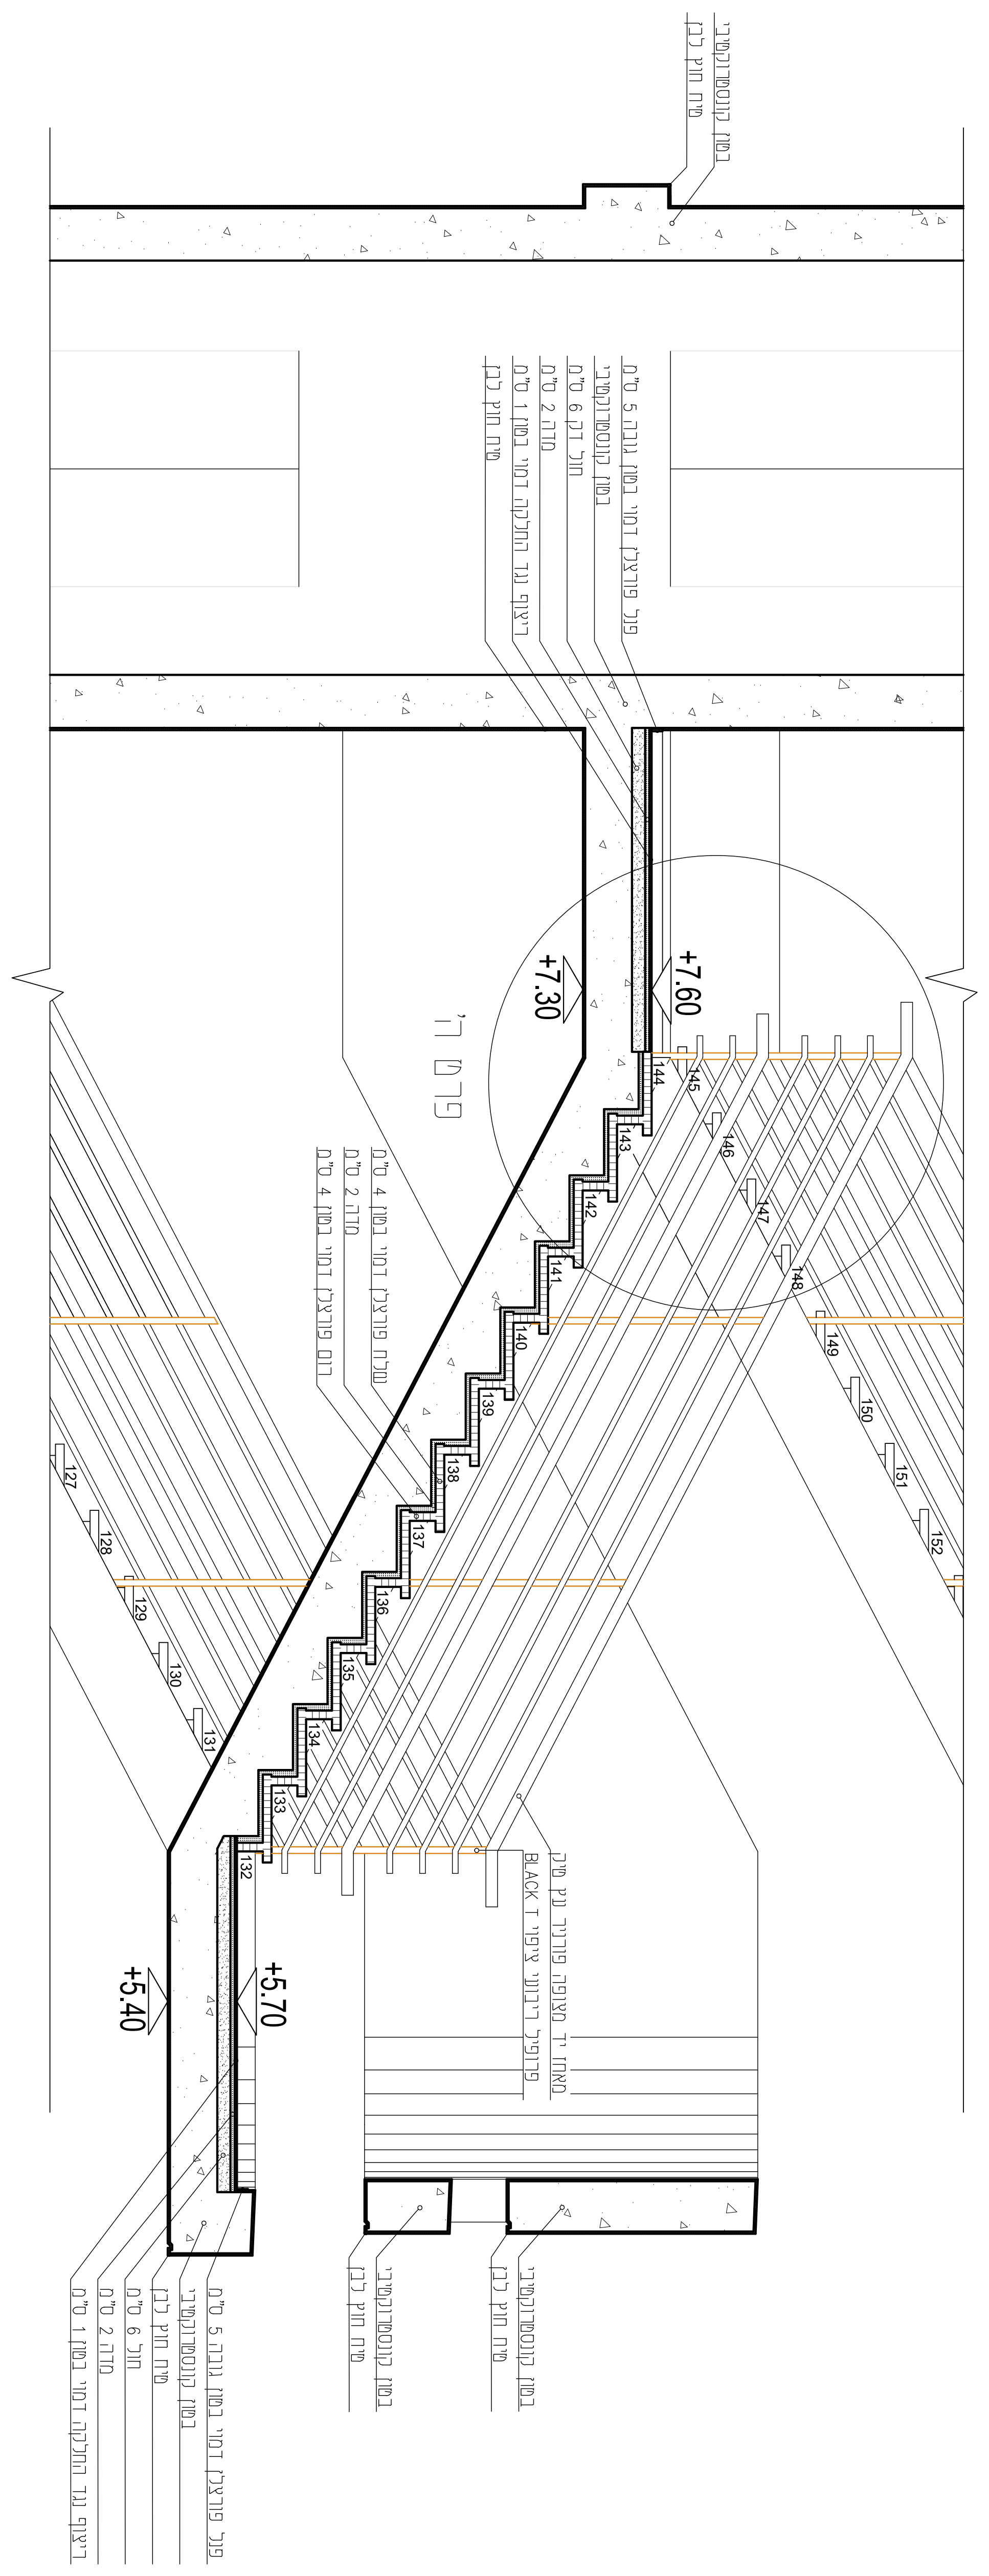

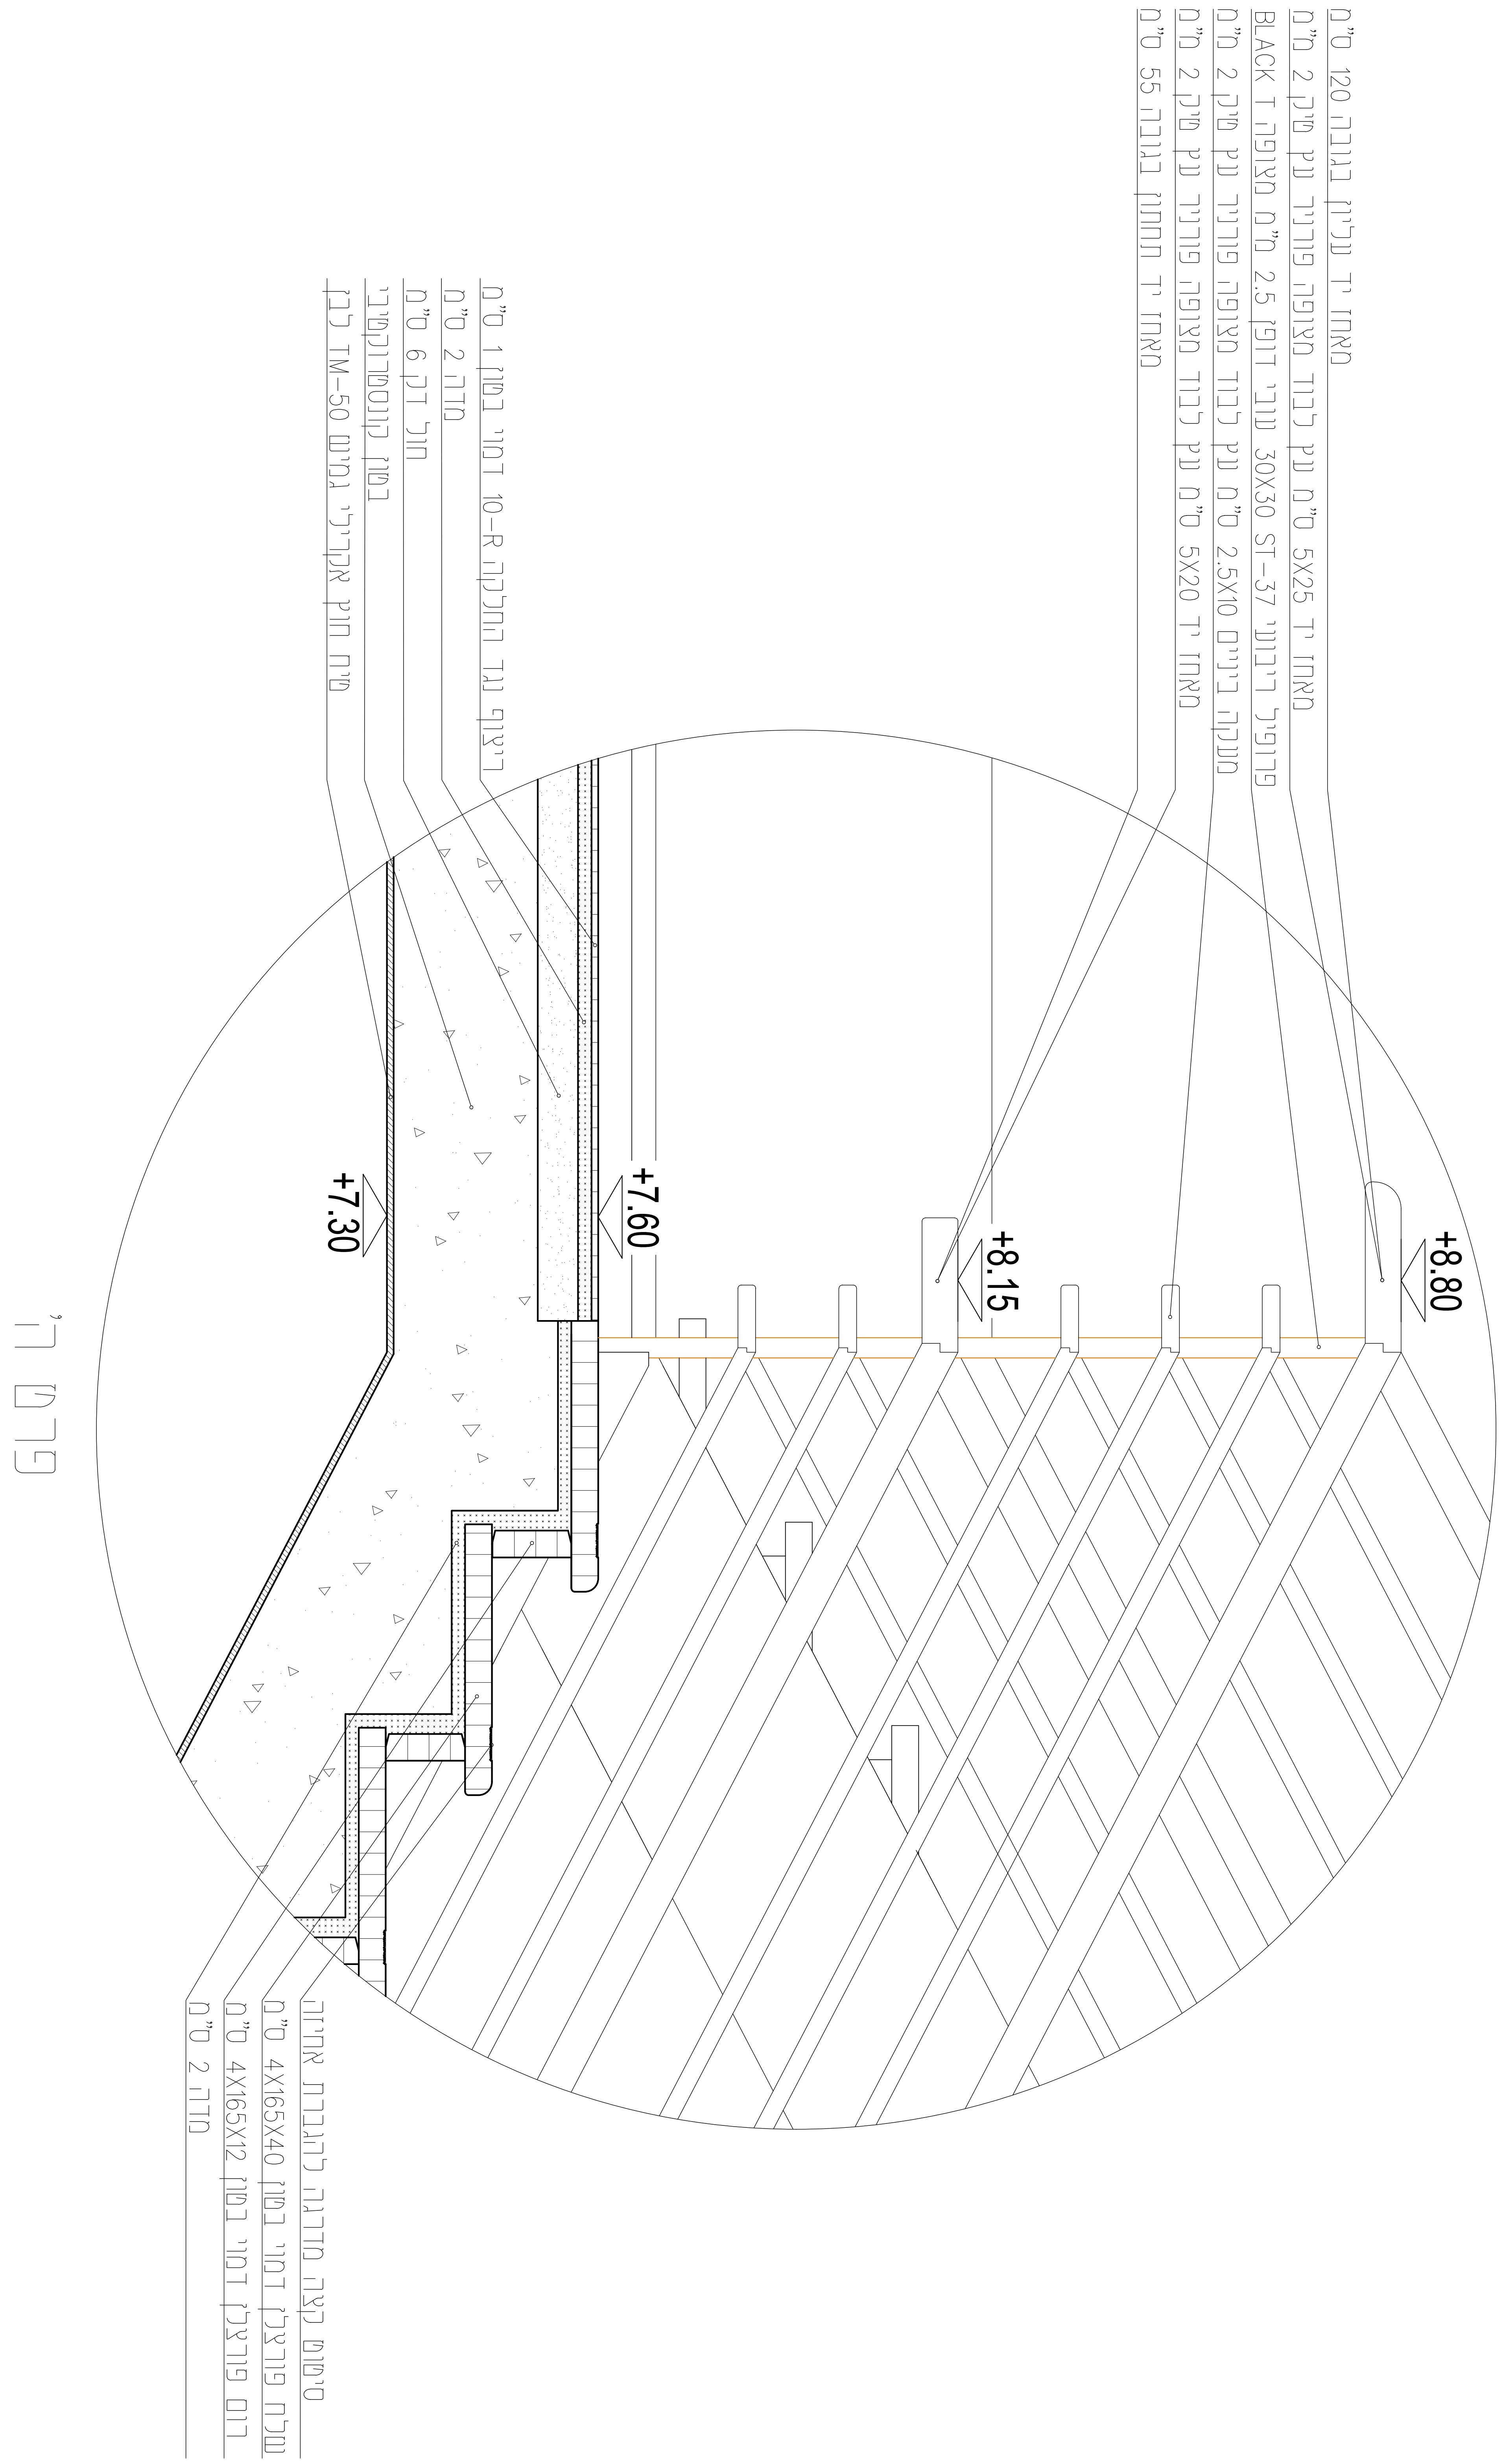
+8.80
+8.15
+7.60
+7.30
מאחז יד עליון בגובה 120 ס"מ
מאחז יד 5X25 ס"מ עץ לבוד מצופה פורניר עץ טיק 2 מ"מ
פרופיל ריבועי ST-37 30X30 עובי דופן 2.5 מ"מ מצופה BLACK T
מעקה ביניים 2.5X10 ס"מ עץ לבוד מצופה פורניר עץ טיק 2 מ"מ
מאחז יד 5X20 ס"מ עץ לבוד מצופה פורניר עץ טיק 2 מ"מ
מאחז יד תחתון בגובה 55 ס"מ
ריצוף נגד החלקה R-10 דמוי בטון 1 ס"מ
מדה 2 ס"מ
חול דק 6 ס"מ
בטון קונסטרוקטיבי
טיח חוץ אקרילי גמיש TM-50 לבן
סיטום קצה מדרגה להגברת אחיזה
שלח פורצלן דמוי בטון 4X165X40 ס"מ
רום פורצלן דמוי בטון 4X165X12 ס"מ
מדה 2 ס"מ

פרט ה'